


KARIBA SOLAR PLANT BATHYMETRIC SURVEY LAYOUT

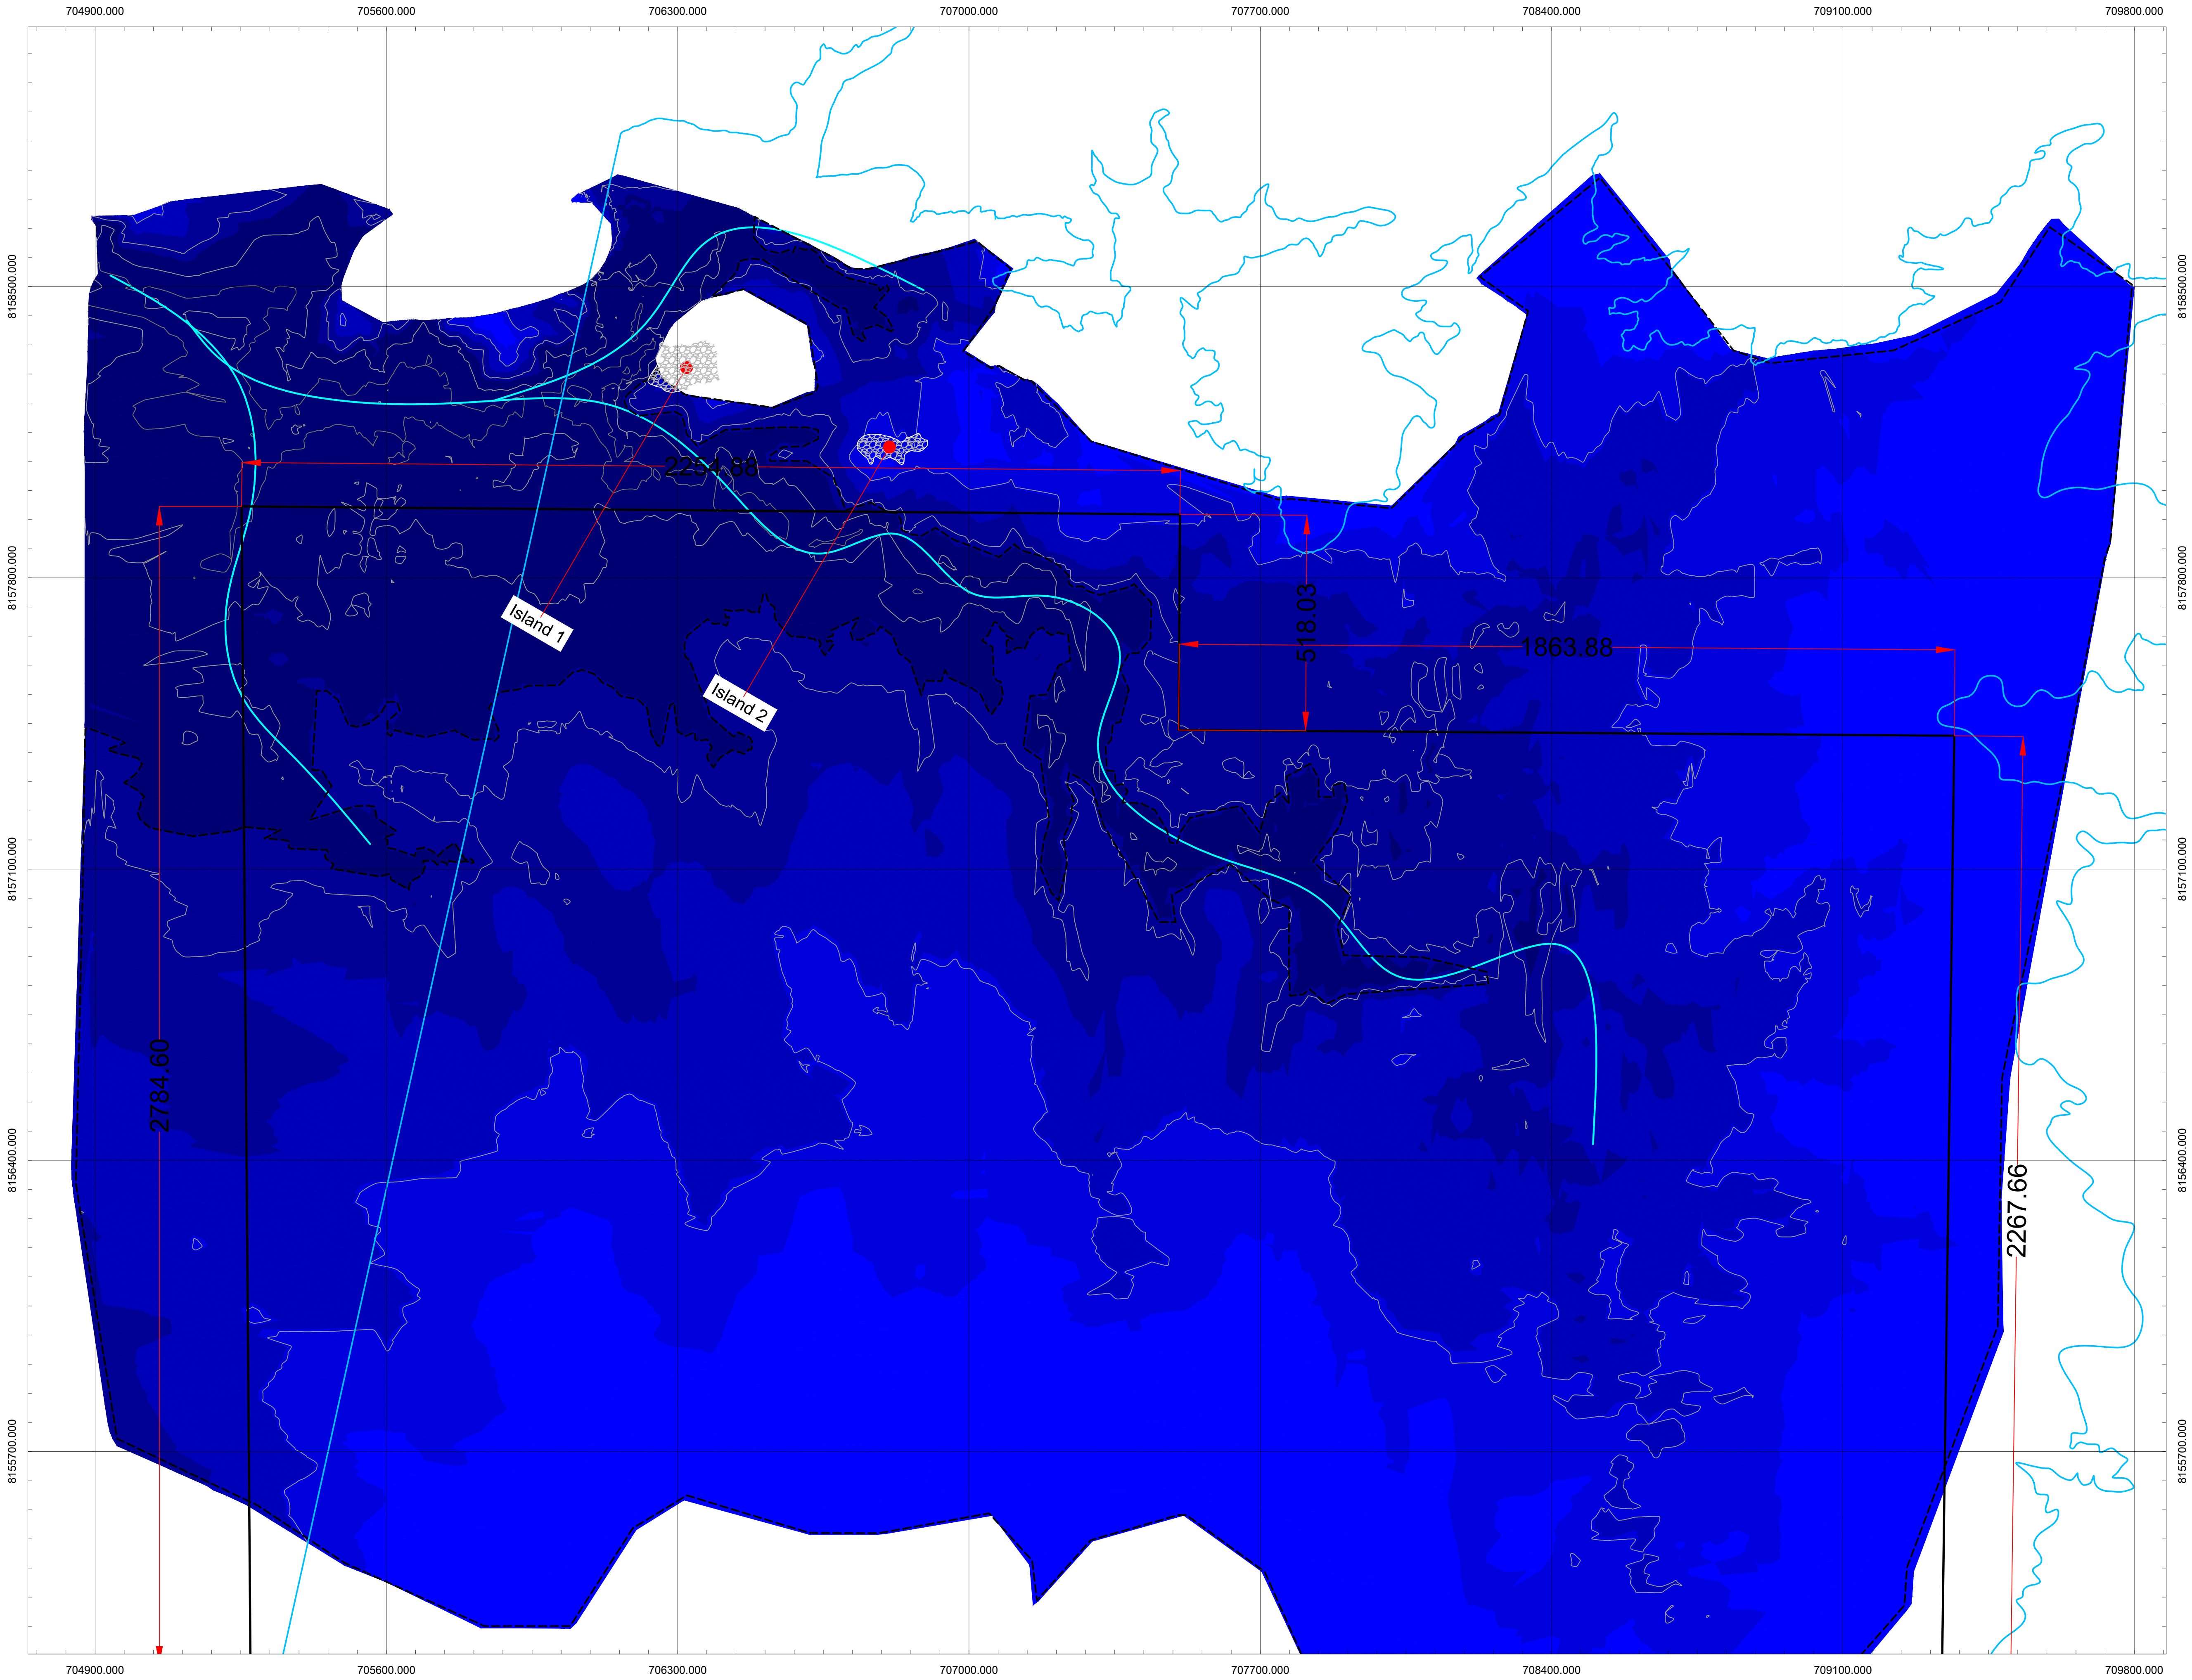

REVISIONS & COMMENTS				
REV	DESCRIPTION NOTES			BY:
N.A	1. Plan Scale 1:7500 2. Contours are at 5m interval. 3. The most suitable solar installation region has depth range from 5.00 - 16.52m. Key Informatics (Pvt) Ltd Sustainable solutions for energy, water & environment			GSE
N.A				GSE
N.A				GSE
N.A	Key Informatics (Pvt) Ltd Sustainable solutions for energy, water & environment			GSE
N.A				GSE
N.A				GSE
PROJECT LOCATION: KARIBA, MASHONALAND WEST PROVINCE				
Geodetic engineering		COMPANY PROFILE		
		FIRM NAME	Geodetic Surveying & Engineering (Pvt) Ltd.	
		EMAIL ADDRESS	info@geodetic.co.zw	
GSE	GSE	GSE	ADDRESS	No.3802 Nhoru Rd Old Winsor, Ruwa
DRAWING TITLE:		BATHYMETRIC SURVEY DEPTH SUITABILITY MAP		
CLIENT:		GREEN HYDRID POWER (PVT) LTD		
COORDINATE SYSTEM				
REFERENCE DATUM		World Geodetic System 1984 (WGS84)		
PROJECTION		Universal Transverse Mercator (UTM)		
ZONE		35S		
DEPTH ANALYSIS LEGEND				
DEPTH RANGE (m)		COLOR		
5.00 - 8.17				
8.17 - 10.13				
10.13 - 12.64				
12.64 - 16.52				
16.52 - 24.63				
TOPOGRAPHY LEGEND				
Suitable Solar Plant Installation Region				
Shoreline				
Contours		475.00 470.00		
DATE: MARCH 2026	SURVEYED BY: GSE	DRAWN BY: GSE	CHECKED BY: GSE	APPROVED BY: GSE
SHEET NO: 01	DRAWING SCALE AS SHOWN		DRAWING PAPER SIZE: IOS A1	