
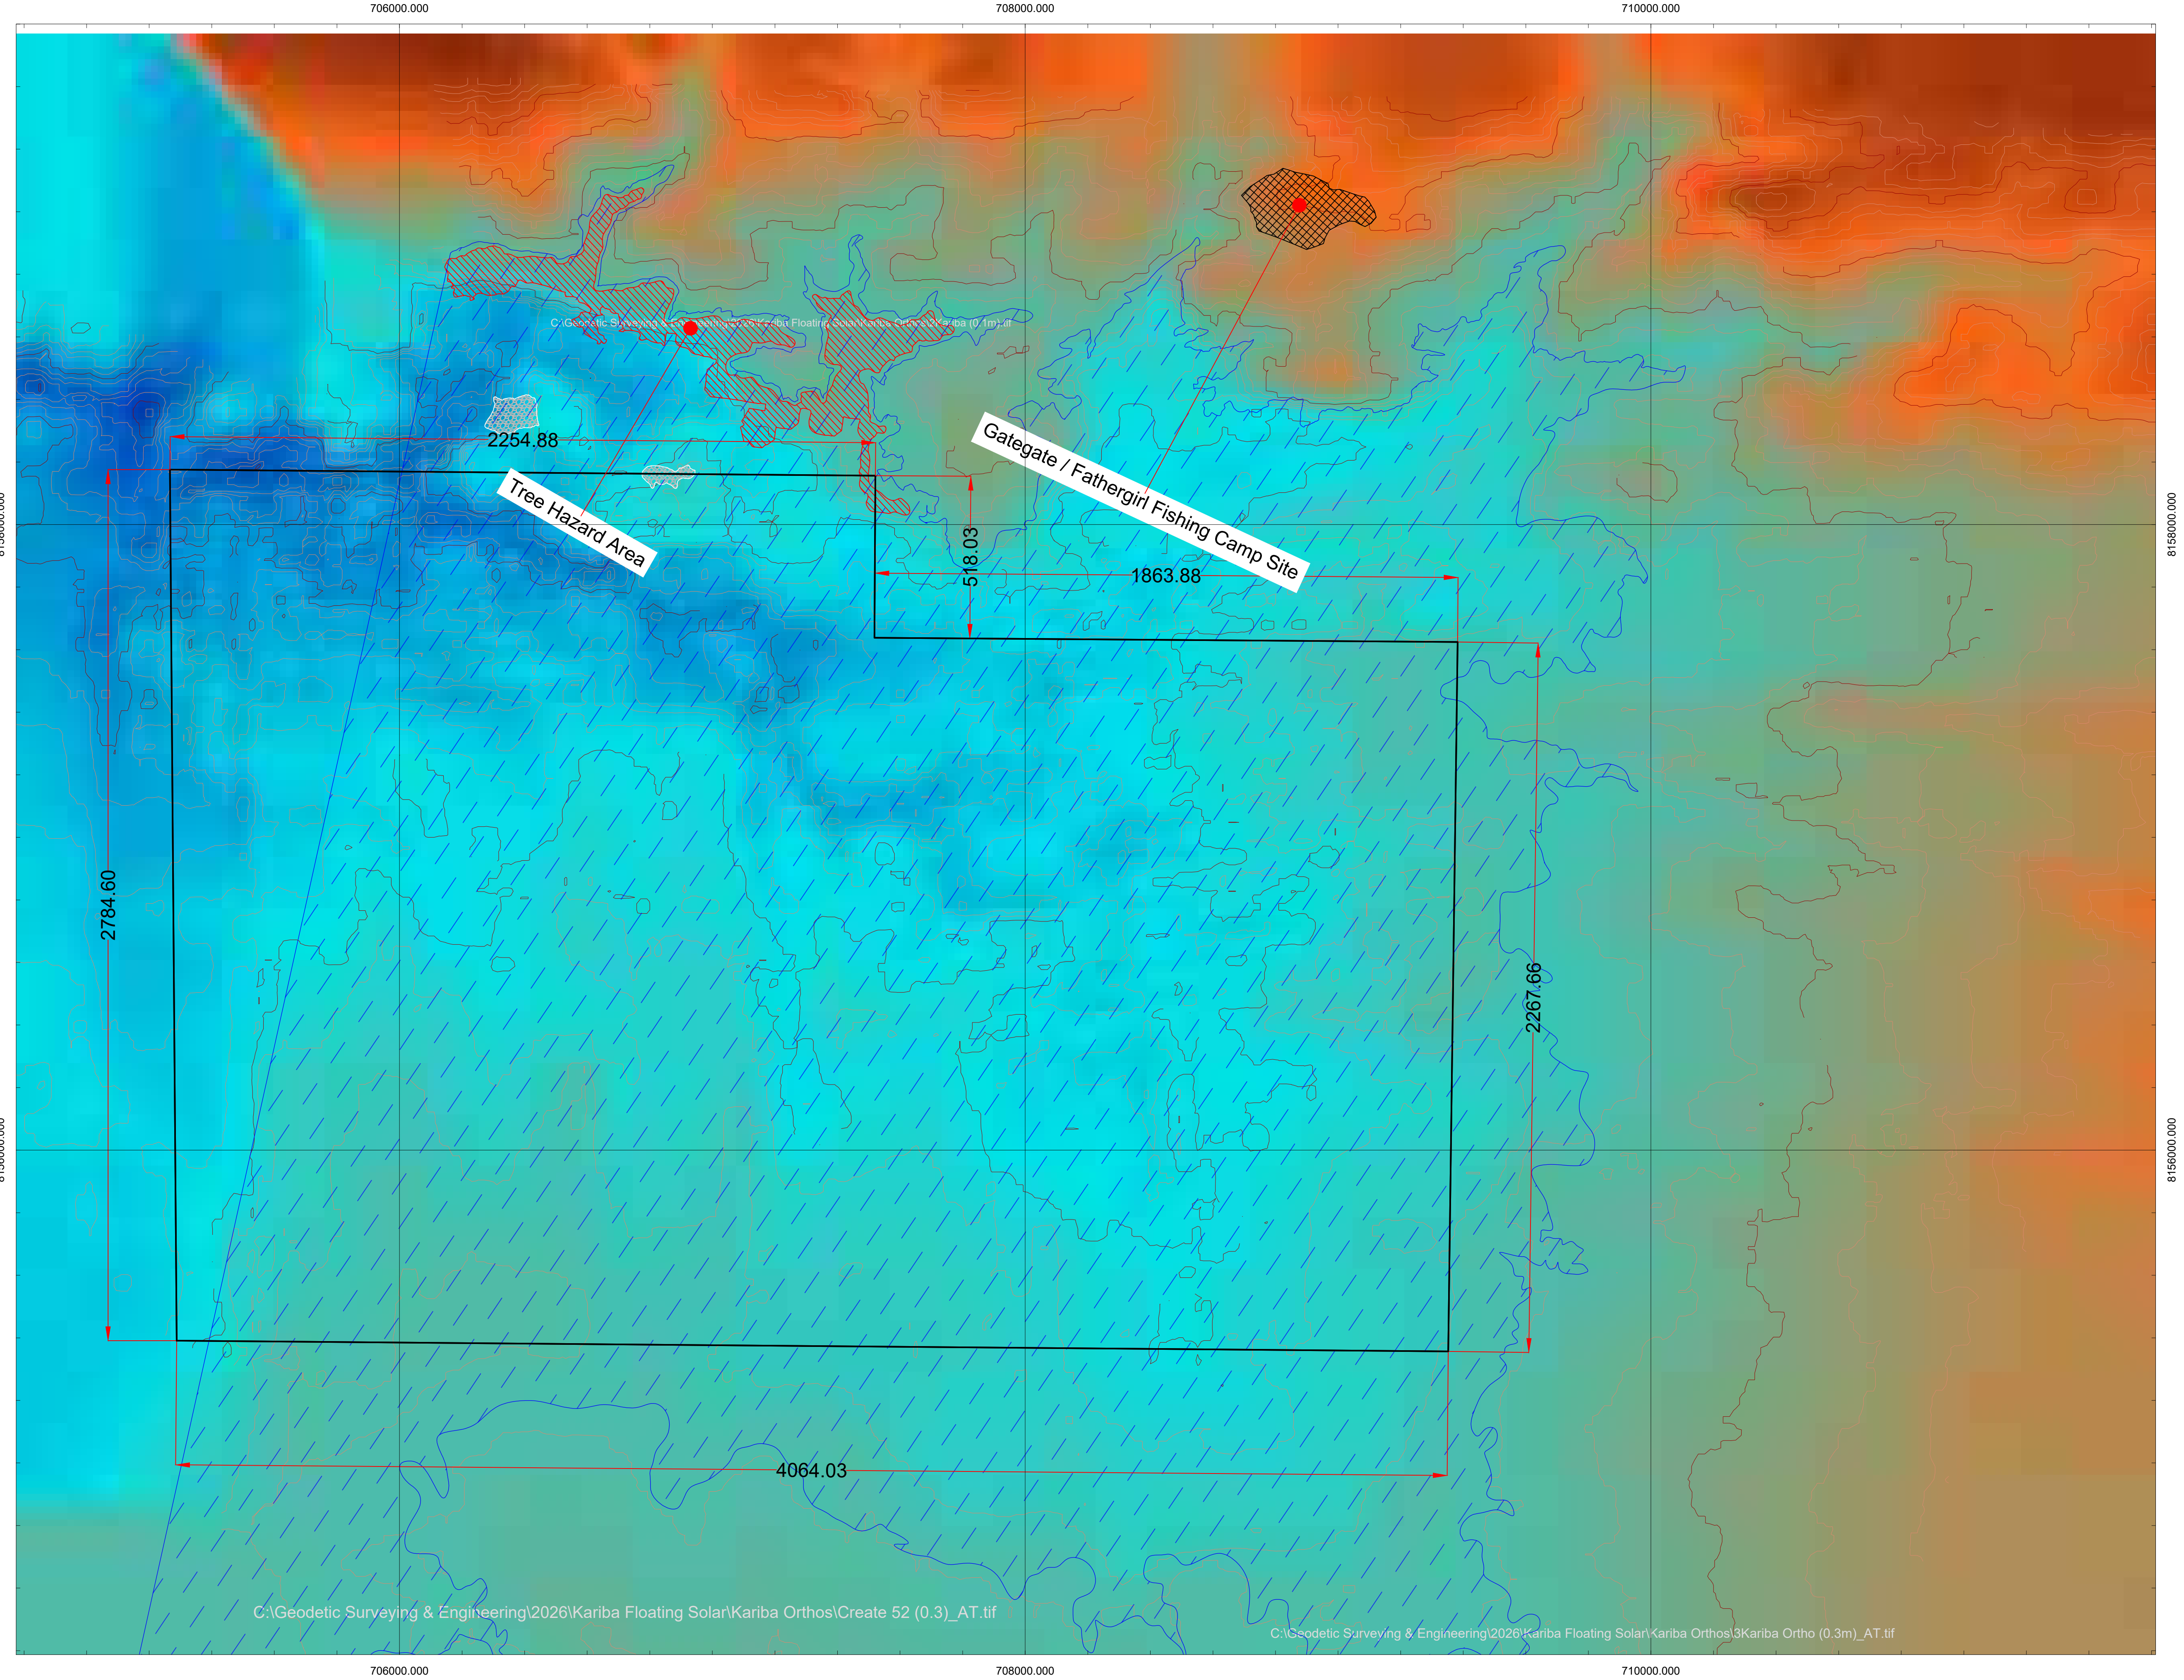


GREEN HYBRID POWER 2 X 500MW FLOATING SOLAR HEIGHT ANALYSIS MAP

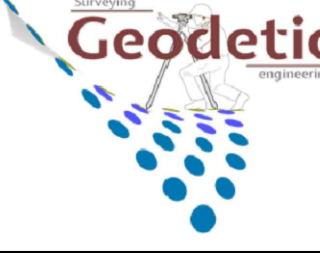

REVISIONS & COMMENTS				
REV	DESCRIPTION NOTES			BY:
N.A	1. Plan Scale 1:15 000 2. Contours are at 1m interval			GSE
N.A				GSE
N.A				GSE
N.A	 Key Informatics (Pvt) Ltd <i>Sustainable solutions for energy, water & environment</i>			GSE
N.A				GSE
N.A				GSE
PROJECT LOCATION: GACHE-GACHE BAY, NYENJE, KARIBA				
		COMPANY PROFILE		
		FIRM NAME	Geodetic Surveying & Engineering (Pvt) Ltd.	
		EMAIL ADDRESS	info@geodetic.co.zw	
GSE	GSE	GSE	ADDRESS	No.3802 Nhoru Rd Old Winsor, Ruwa
DRAWING TITLE:		HEIGHT ANALYSIS MAP		
CLIENT:		GREEN HYBRID POWER (PVT) LTD		
COORDINATE SYSTEM				
REFERENCE DATUM		World Geodetic System 1984 (WGS84)		
PROJECTION		Universal Transverse Mercator (UTM)		
ZONE		35S		